


<<< NEIGHBOUR PLOT >>>

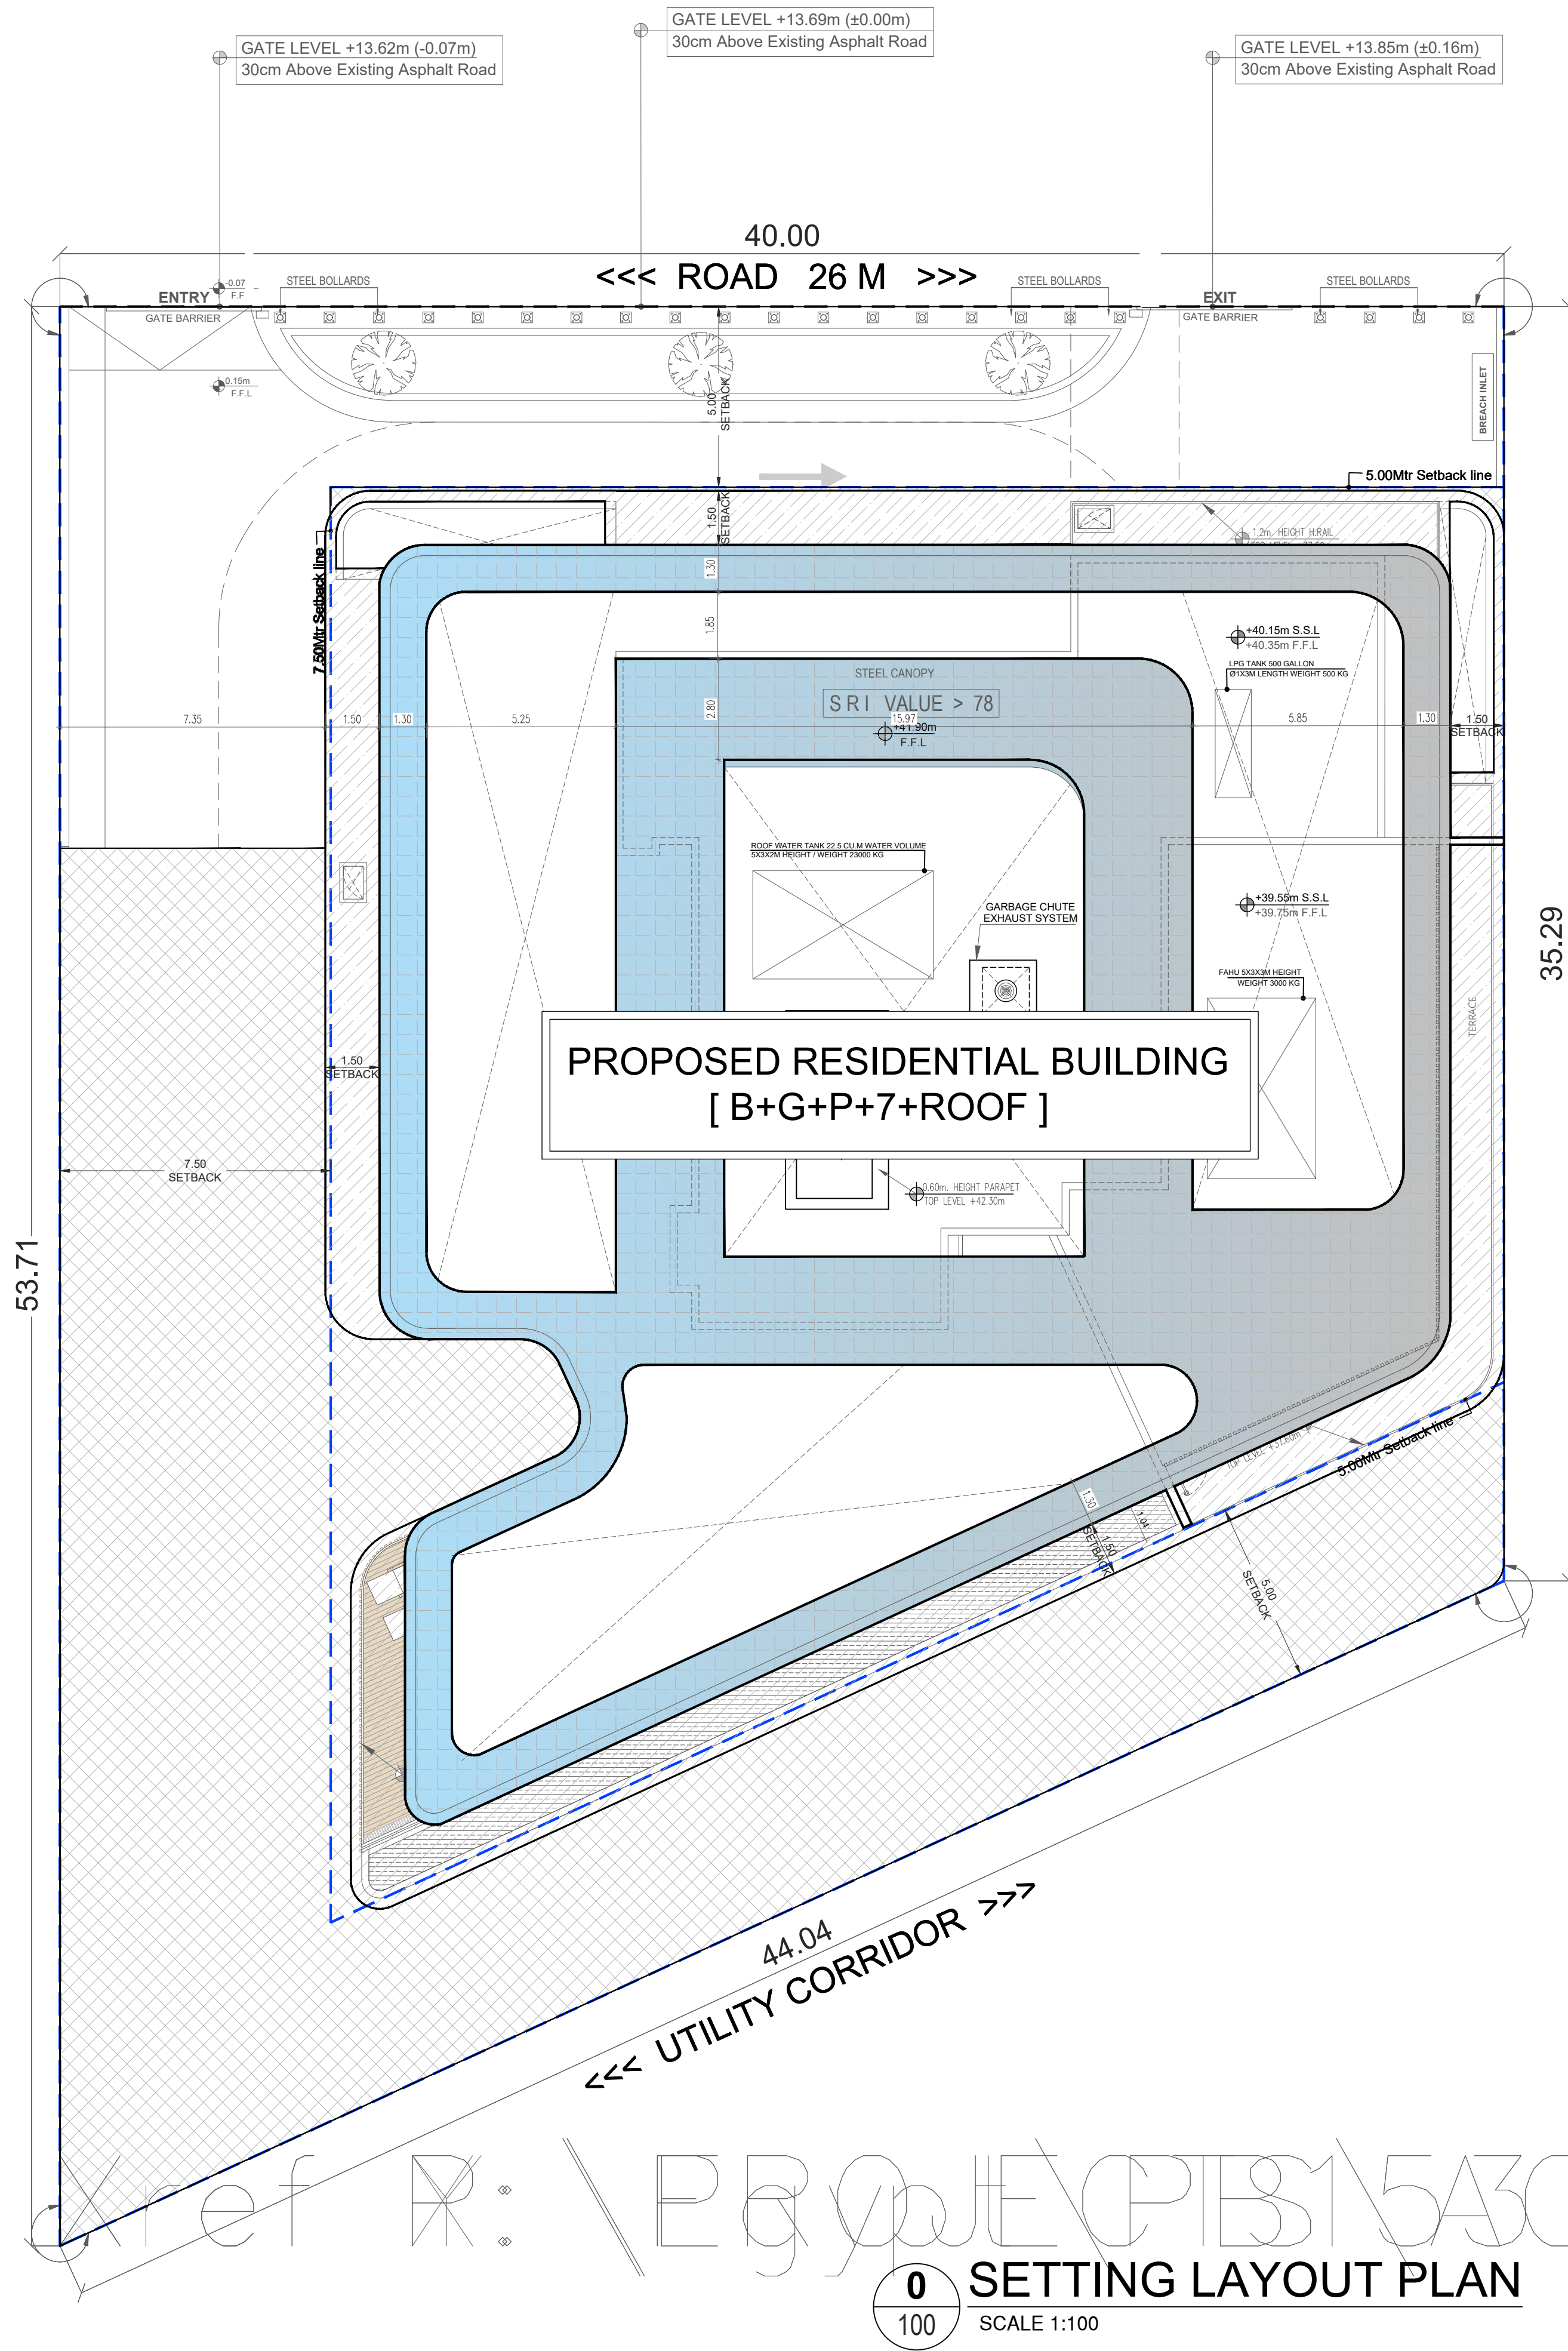


0 SETTING LAYOUT PLAN
100 SCALE 1:100

<<< LANDSCAPE >>>

Paving Specifications شروط ومواصفات الأرصفة	
Tiles بلاط الأرصفة	
Footpaths: 10x20x6cm red rectangular interlock tiles. Reinstate using the same type of old existing tiles. Use the pattern provided by the Road Consultant. Parking, Drive Way and Vehicular Access: 10x20x8cm gray color rectangle interlock tiles. Reinstate using the same type of old existing paving.	رصف المشاة والمسك وبلاط الأرصفة: بلاط 10x20x6cm أحمر اللون 6mm لثوب 10x20x6cm. إعادة التركيب باستخدام نفس نوع بلاط الأرصفة الذي كان قديماً. استخدام النمط المتاح من قبل الاستشاري للطرق. الوقوف، طريق السيارة وإتاحة الوصول إلى مواقف السيارات: بلاط 10x20x8cm رمادي اللون 8mm لثوب 10x20x8cm. إعادة التركيب باستخدام نفس نوع بلاط الأرصفة الذي كان قديماً.
Kerbs (Precast HD) أحجار حواف الأرصفة	
Provide up stand kerb in between footpath and parking and in between footpath and vehicular access. Provide dropped kerb between the (existing or proposed) asphalt edge and parking area, and between the (existing or proposed) asphalt edge and vehicular access. Provide heel kerb at the edge of subbase and between footpath and plantation area.	تركيب أحجار حالة الأرصفة كاملة بين رصف المشاة والمواقف وبين رصف المشاة ومداخل السيارات. تركيب أحجار حالة الأرصفة ثلثة بين حالة الأرصفة (القائمة أو المقترحة) ومداخل المواقف وكذلك بين حالة الأرصفة (القائمة أو المقترحة) ومداخل المواقف. وضع Heel Kerb على حافة المسك بين رصف المشاة ومنطقة الزراعة.
Traffic Signs علامات السيارات	
At vehicular exit install DM Road Sign No. 301 (no entry sign) from the building side, and DM Road Sign No. 304 (no entry sign) from the road side.	بم تركيب إشارة الطرق رقم 301 (عدم الدخول) عند مخرج السيارات من جهة المبنى وإشارة الطرق رقم 304 (عدم دخول) من جهة الطريق.
General Conditions شروط عامة	
1. Footpath shall be 15 cm above asphalt edge. 2. Once plants shall be within 15 cm above footpath, or within 30 cm above asphalt edge. 3. First step on plot line shall be within 15 cm above foot path/parking paving. 4. Contractor/owner shall contact all concerned authorities and obtain their NOCs, before committing excavations and before removing or leveling any MHT, gutters, manholes, streetlights poles, etc. all before starting works. 5. Paved area shall remain open to public at all times and shall not be reserved or blocked using bollards/chains, etc. at any time. 6. No plantation is permitted under this NOC. 7. The tiles shall be approved as per DM local order 44/90, and to be fixed as per the approved drawings. 8. All kerb stones shall be painted in black and white - only at vehicular exit is continuous white, proper and adequate traffic signs and proper road markings shall be installed, wherever required. 9. Contractor/owner shall provide adequate storm water drainage system for the paved area as per the approval of DM (Drainage Department) as per the attached standard sketch. 10. All existing manholes shall remain exposed and accessible at all times. 11. All existing manholes must be leveled as per the proposed paving level with prior NOCs from the concerned authorities. 12. Paving works shall be as per the attached approved sketch/drawings and conditions.	1. أن ارتفاع رصف المشاة 15 سم عن مستوى حافة الأرصفة. 2. أن ارتفاع سطح السيارات 15 سم عن مستوى الرصيف، أو 30 سم عن حافة الأرصفة. 3. يكون المنسوب الأول درجة في المبنى أعلى من الرصيف بمقدار 15 سم. 4. يتعين المنسوب على سيارات المصاحبة مع المصاحبة من جميع الجهات المختصة قبل البدء بأعمال الرصف، وقبل البدء في رفع أو إزالة أو تحويل أية عروة تقاسم في مداخل، أصدرت إقراراً، فائدتا جميع الجهات المختصة، لا يجوز وضع أسدنة وسلاسل حجز لمكان الرصيف لتوليد السيارات. 5. لا يسمح بإقامة الحائجة بناء على حافة الأرصفة (القائمة أو المقترحة) أو الرصيف، يجب أن تكون مطابقة للمواصفات بنية تسي وفقاً لنشر المصاحبة، رقم 90/44 ولا يتم تركيبها وفقاً للرصيف المصاحبة. 6. على المالك منع جميع أحجار الرصيف بالأبيض والأسود، مع صيغتها باللون الأبيض المستمر عند مداخل ومخارج المداخل، وكذلك تركيب علامات المرور والعلامات المرورية المناسبة بمداخل ومخارج المداخل حسب مواصفات بلدية دبي، على الدوائر (المالك) ترديد شكاية المصاحبة أمام الأمانة العامة للمرور، حسبما تشهده إرادة المصاحبة (المصاحبة) ويجب إكمال الشكاية فوراً. 7. يجب أن يثبت جميع غرف غسيل الخدمات مكتوبة للبيان وملائمة للرصيف إليها في جميع الأوقات. 8. يجب تشييد جميع غرف الغسيل القائمة ببنائها في غرضها حسب المنسوب المصاحبة، لا تضاف مع المصاحبة على شكايات عدم المصاحبة من جميع الجهات المختصة. 9. يجب إكمال الرصيف حسب التخطيط المصاحبة والالتزام بالمشروطات.

NOTES FOR SETTING OUT PLAN

- THE PLOT DIMENSIONS INDICATED ON SETTING OUT PLAN ARE BASED ON THE AFFECTION PLAN RECEIVED FROM THE AUTHORITIES. THE CONTRACTOR SHALL OBTAIN NECESSARY DEMARCATION FROM RELEVANT AUTHORITIES & IN CASE OF ANY DISCREPANCIES, BRING TO THE KNOWLEDGE OF ENGINEER PRIOR TO COMMENCEMENT OF WORK.
- THE PAVEMENT WORKS SHOWN OUTSIDE THE PLOT LIMITS ARE TENTATIVE. THE CONTRACTOR SHALL VERIFY THE DESIGN, DIMENSIONS & LAYOUT WITH RELEVANT AUTHORITIES PRIOR TO COMMENCEMENT OF WORK.
- THE GATE LEVELS GIVEN ON DRAWING HAVE BEEN WORKED OUT BASED ON LEVEL INFORMATION RECEIVED FROM THE AUTHORITIES. THE CONTRACTOR SHALL RECONFIRM THE SAME WITH THE RELEVANT AUTHORITIES PRIOR TO COMMENCEMENT OF WORK.

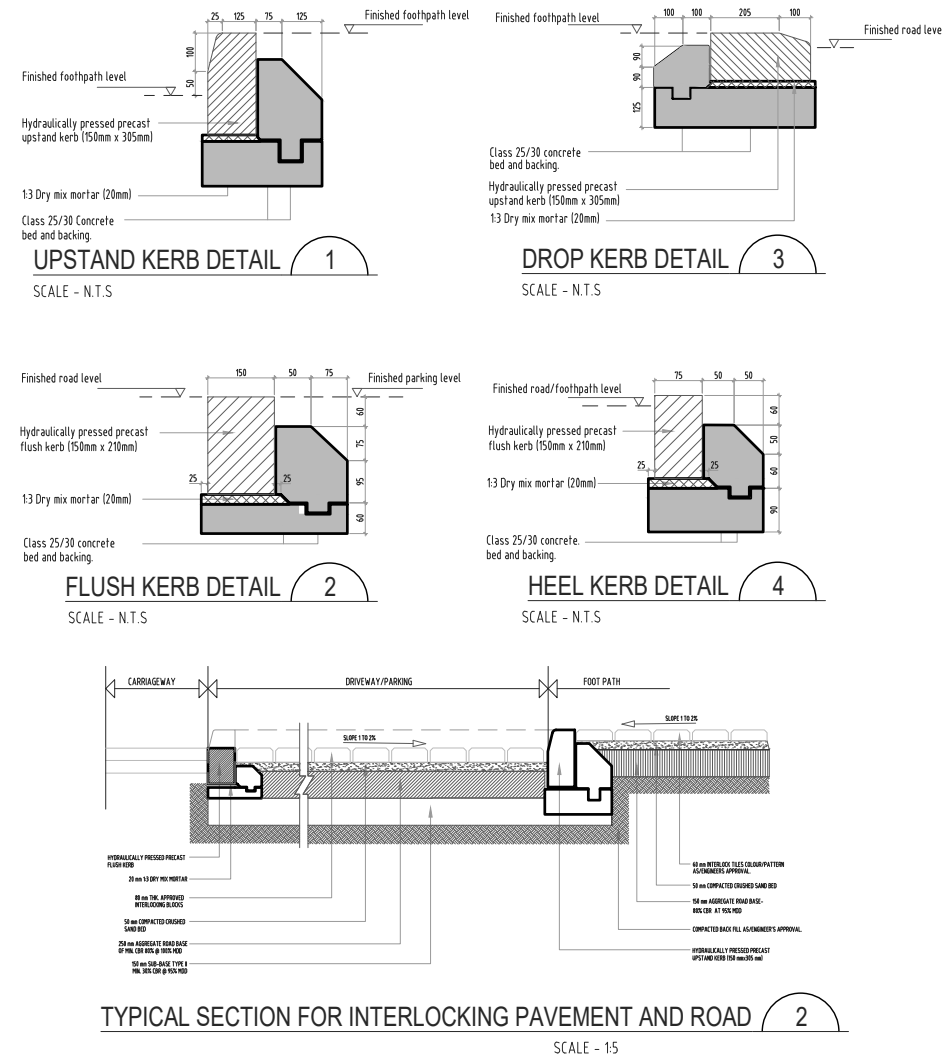

GATE LEVEL IS 30cm ABOVE THE LEVEL OF THE ASPHALTED ROAD

NOTE : ALL EXTERNAL ROAD & PAVEMENT PROFILES SHOWN ON DRAWING SHALL BE SUBJECT TO APPROVAL OF ROAD DEPT., DUBAI MUNICIPALITY

NOTES:

- THIS DRAWING IS THE PROPERTY OF : POE ENGINEERING CONSULTANTS P.O.Box 97046, DUBAI. IT IS FORBIDDEN TO PRODUCE IT'S CONTENTS IN ANY FORM, EXCEPT FOR THE INTENDED PURPOSE.
- THIS DRAWING IS NOT TO BE SCALED. THE STATED DIMENSIONS ONLY ARE TO BE CONSIDERED.
- THE DISCREPANCIES ARE TO BE BROUGHT TO THE ATTENTION AND RESOLVED BY PIONEERS OF EXPERTS ENGINEERING CONSULTANT BEFORE COMMENCEMENT OF ANY WORK.

F.R.L. = FINISH ROAD LEVEL
F.P.L. = FOOT PATH LEVEL
F.G.L. = FINISH FLOOR LEVEL
F.F.L. = FINISH GROUND LEVEL
C.L. = CONCRETE LEVEL



No.	ISSUE FOR CONSTRUCTION DESCRIPTION.	12-11-2025 DATE.	SR DRWN.	SM CHKD.
1	ISSUE FOR CONSTRUCTION			

ISSUE FOR CONSTRUCTION



OWNERS
DARSHANA DINESH SONI
MOHAMMAD ADNAN CHOWDHURY MOHAMMAD ABU JAFAR CHOWDHURY
MOHAMMED SALIM HINGORA SALIM AHMED HINGORA

PROJECT PROPOSED RESIDENTIAL BUILDING	
DESIGN HIGHT B+G+P+7+ROOF	CONSTRUCTION B+G+P+7+ROOF
LOCATION ME'AISEM FIRST	PLOT No. 6850752

PRINCIPAL CONSULTANT
POE
ENGINEERING CONSULTANTS

DWG TITLE:
SETTING LAYOUT PLAN

SCALE		DATE NOV - 2025	
Asst./Draft	Chk.Arch.Eng. Chk.Str. Eng.	Islam Elhabashy Momen Haltham	
DRAWING TYPE Architecture	Chk.Ele. Eng. Chk.Mech.Eng.		
PROJECT No. PB-153	DWG No. A-100		Se. No.
PROJECT No. POE/PB-153/2024/A-100			